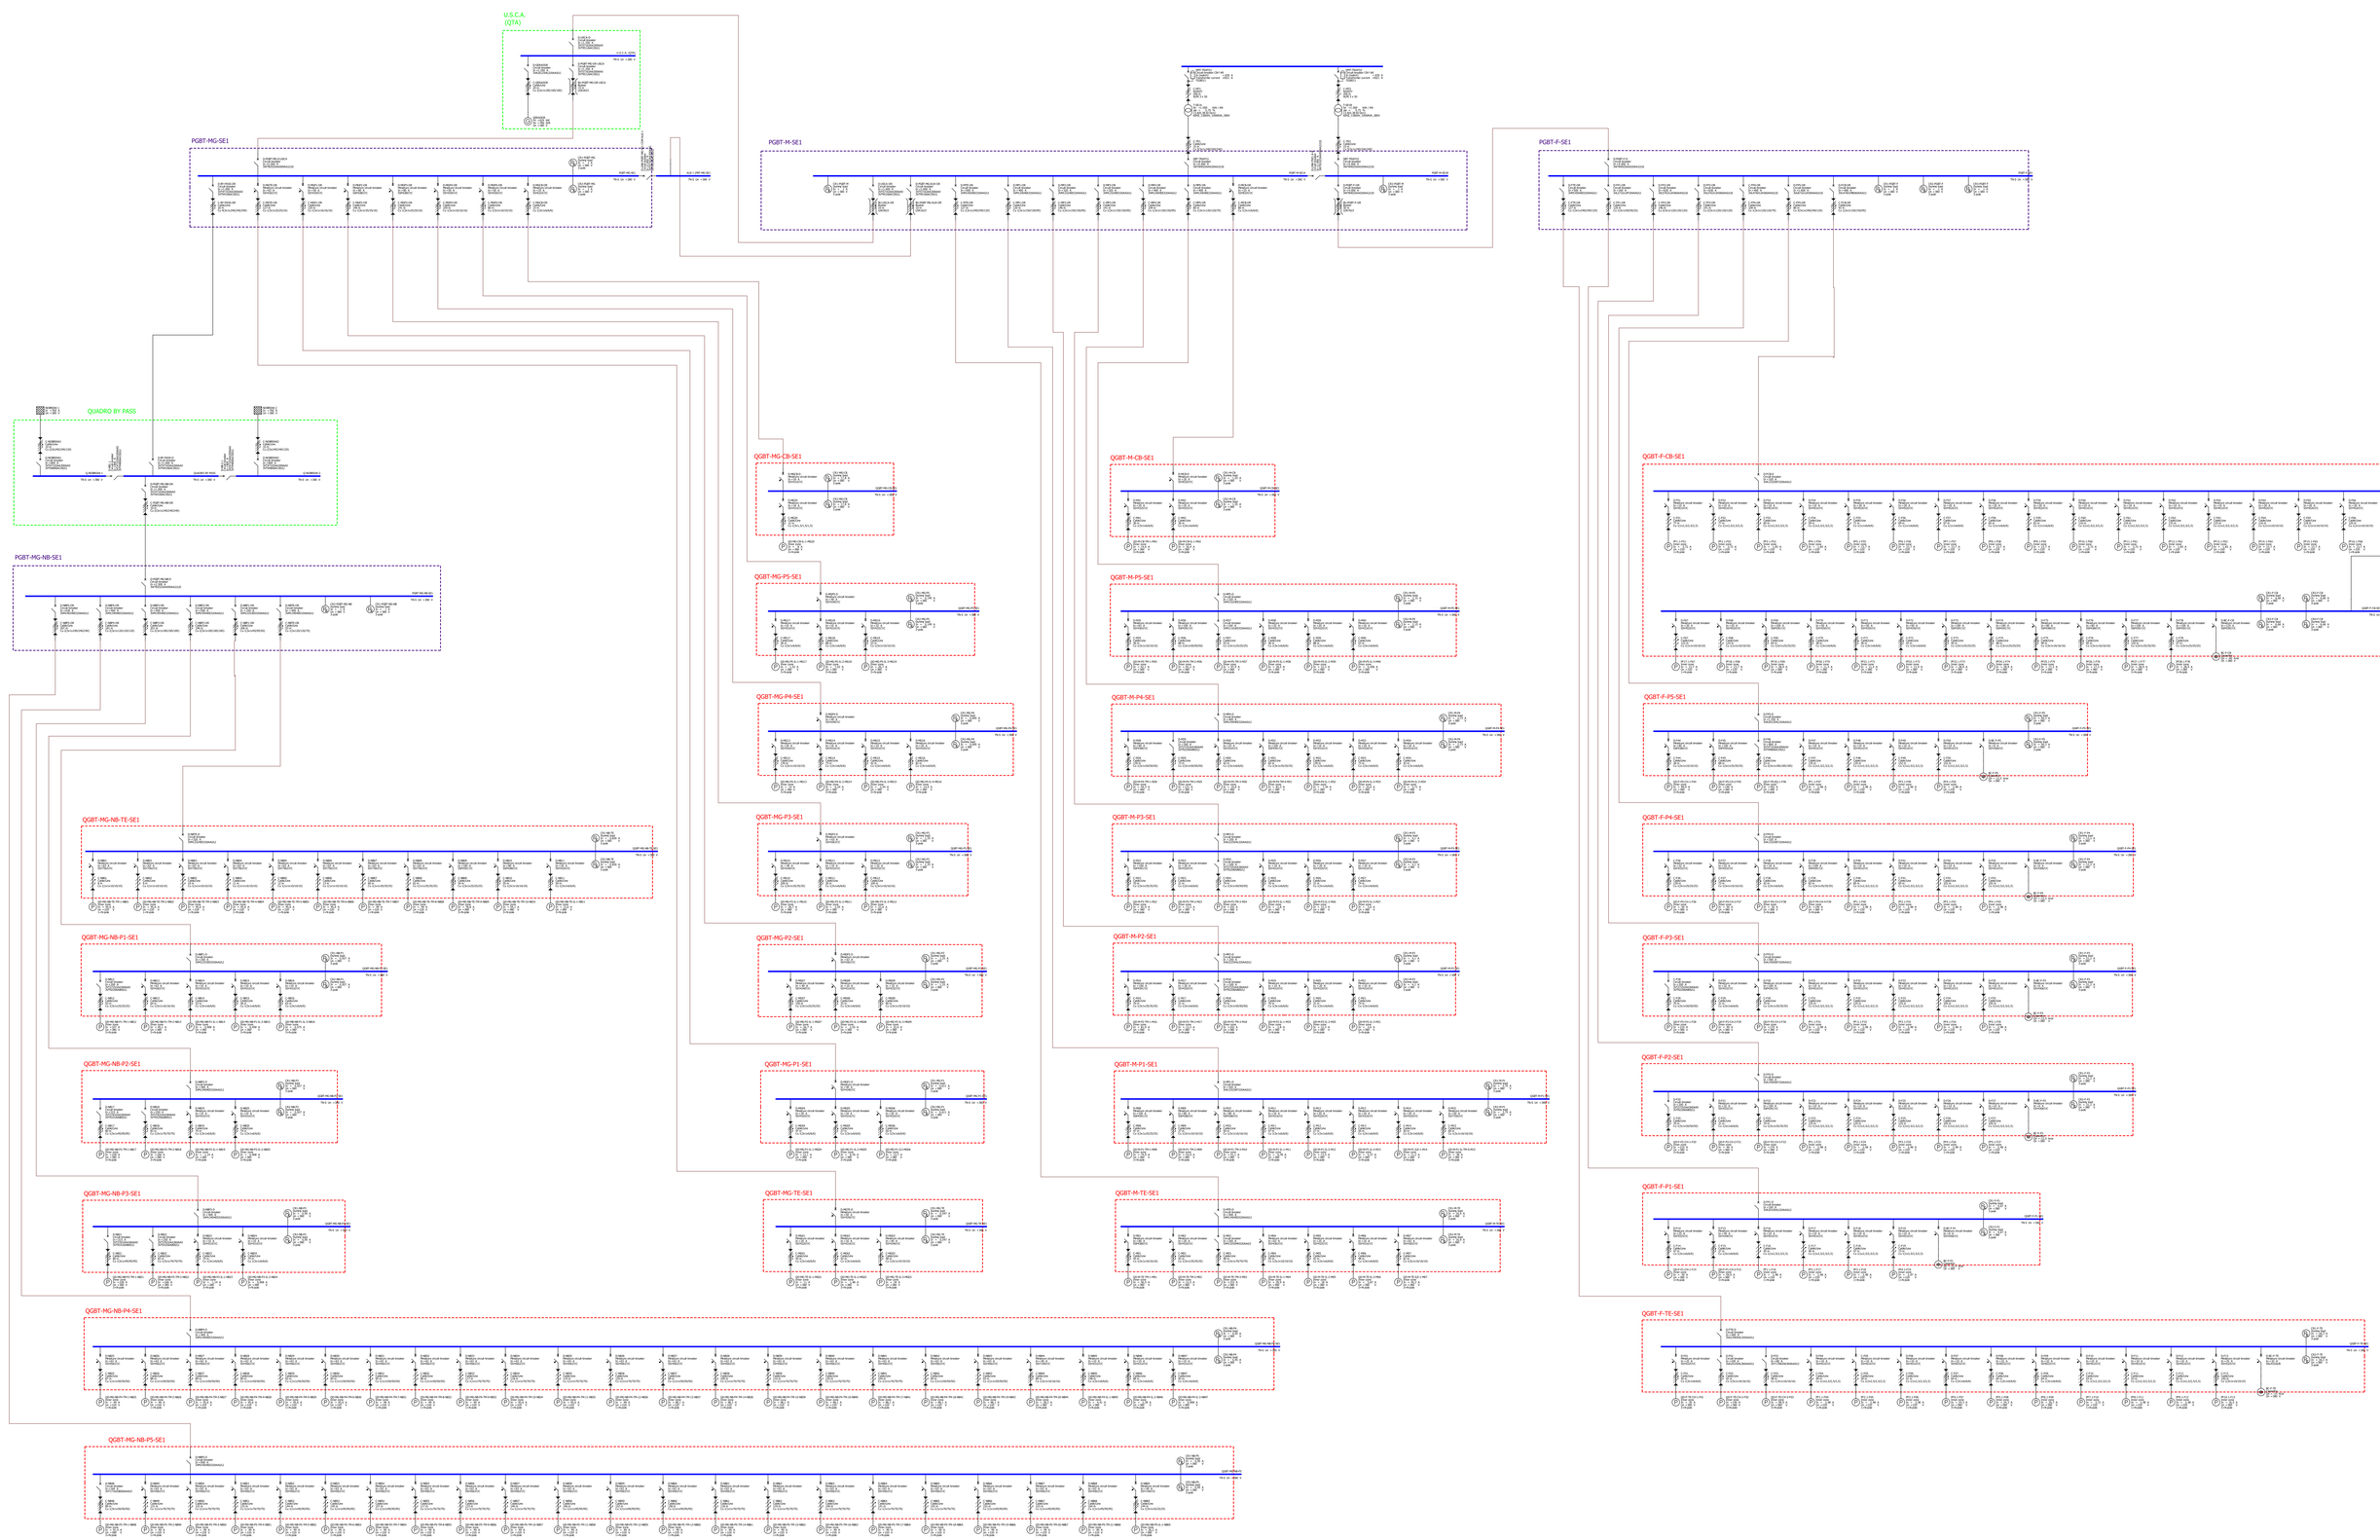

Project name:	Projeto Subestação 8D3U - Ampliação UFU
Engineer:	Jéssica Cristina
Date:	Device parameters
Sheet:	1/1
Design office:	UFU
Location:	Uberlândia
Client:	UFU
Created on:	Jun 14, 2023
Changed on:	Feb 23, 2025

SIMARIS design 3.1.1

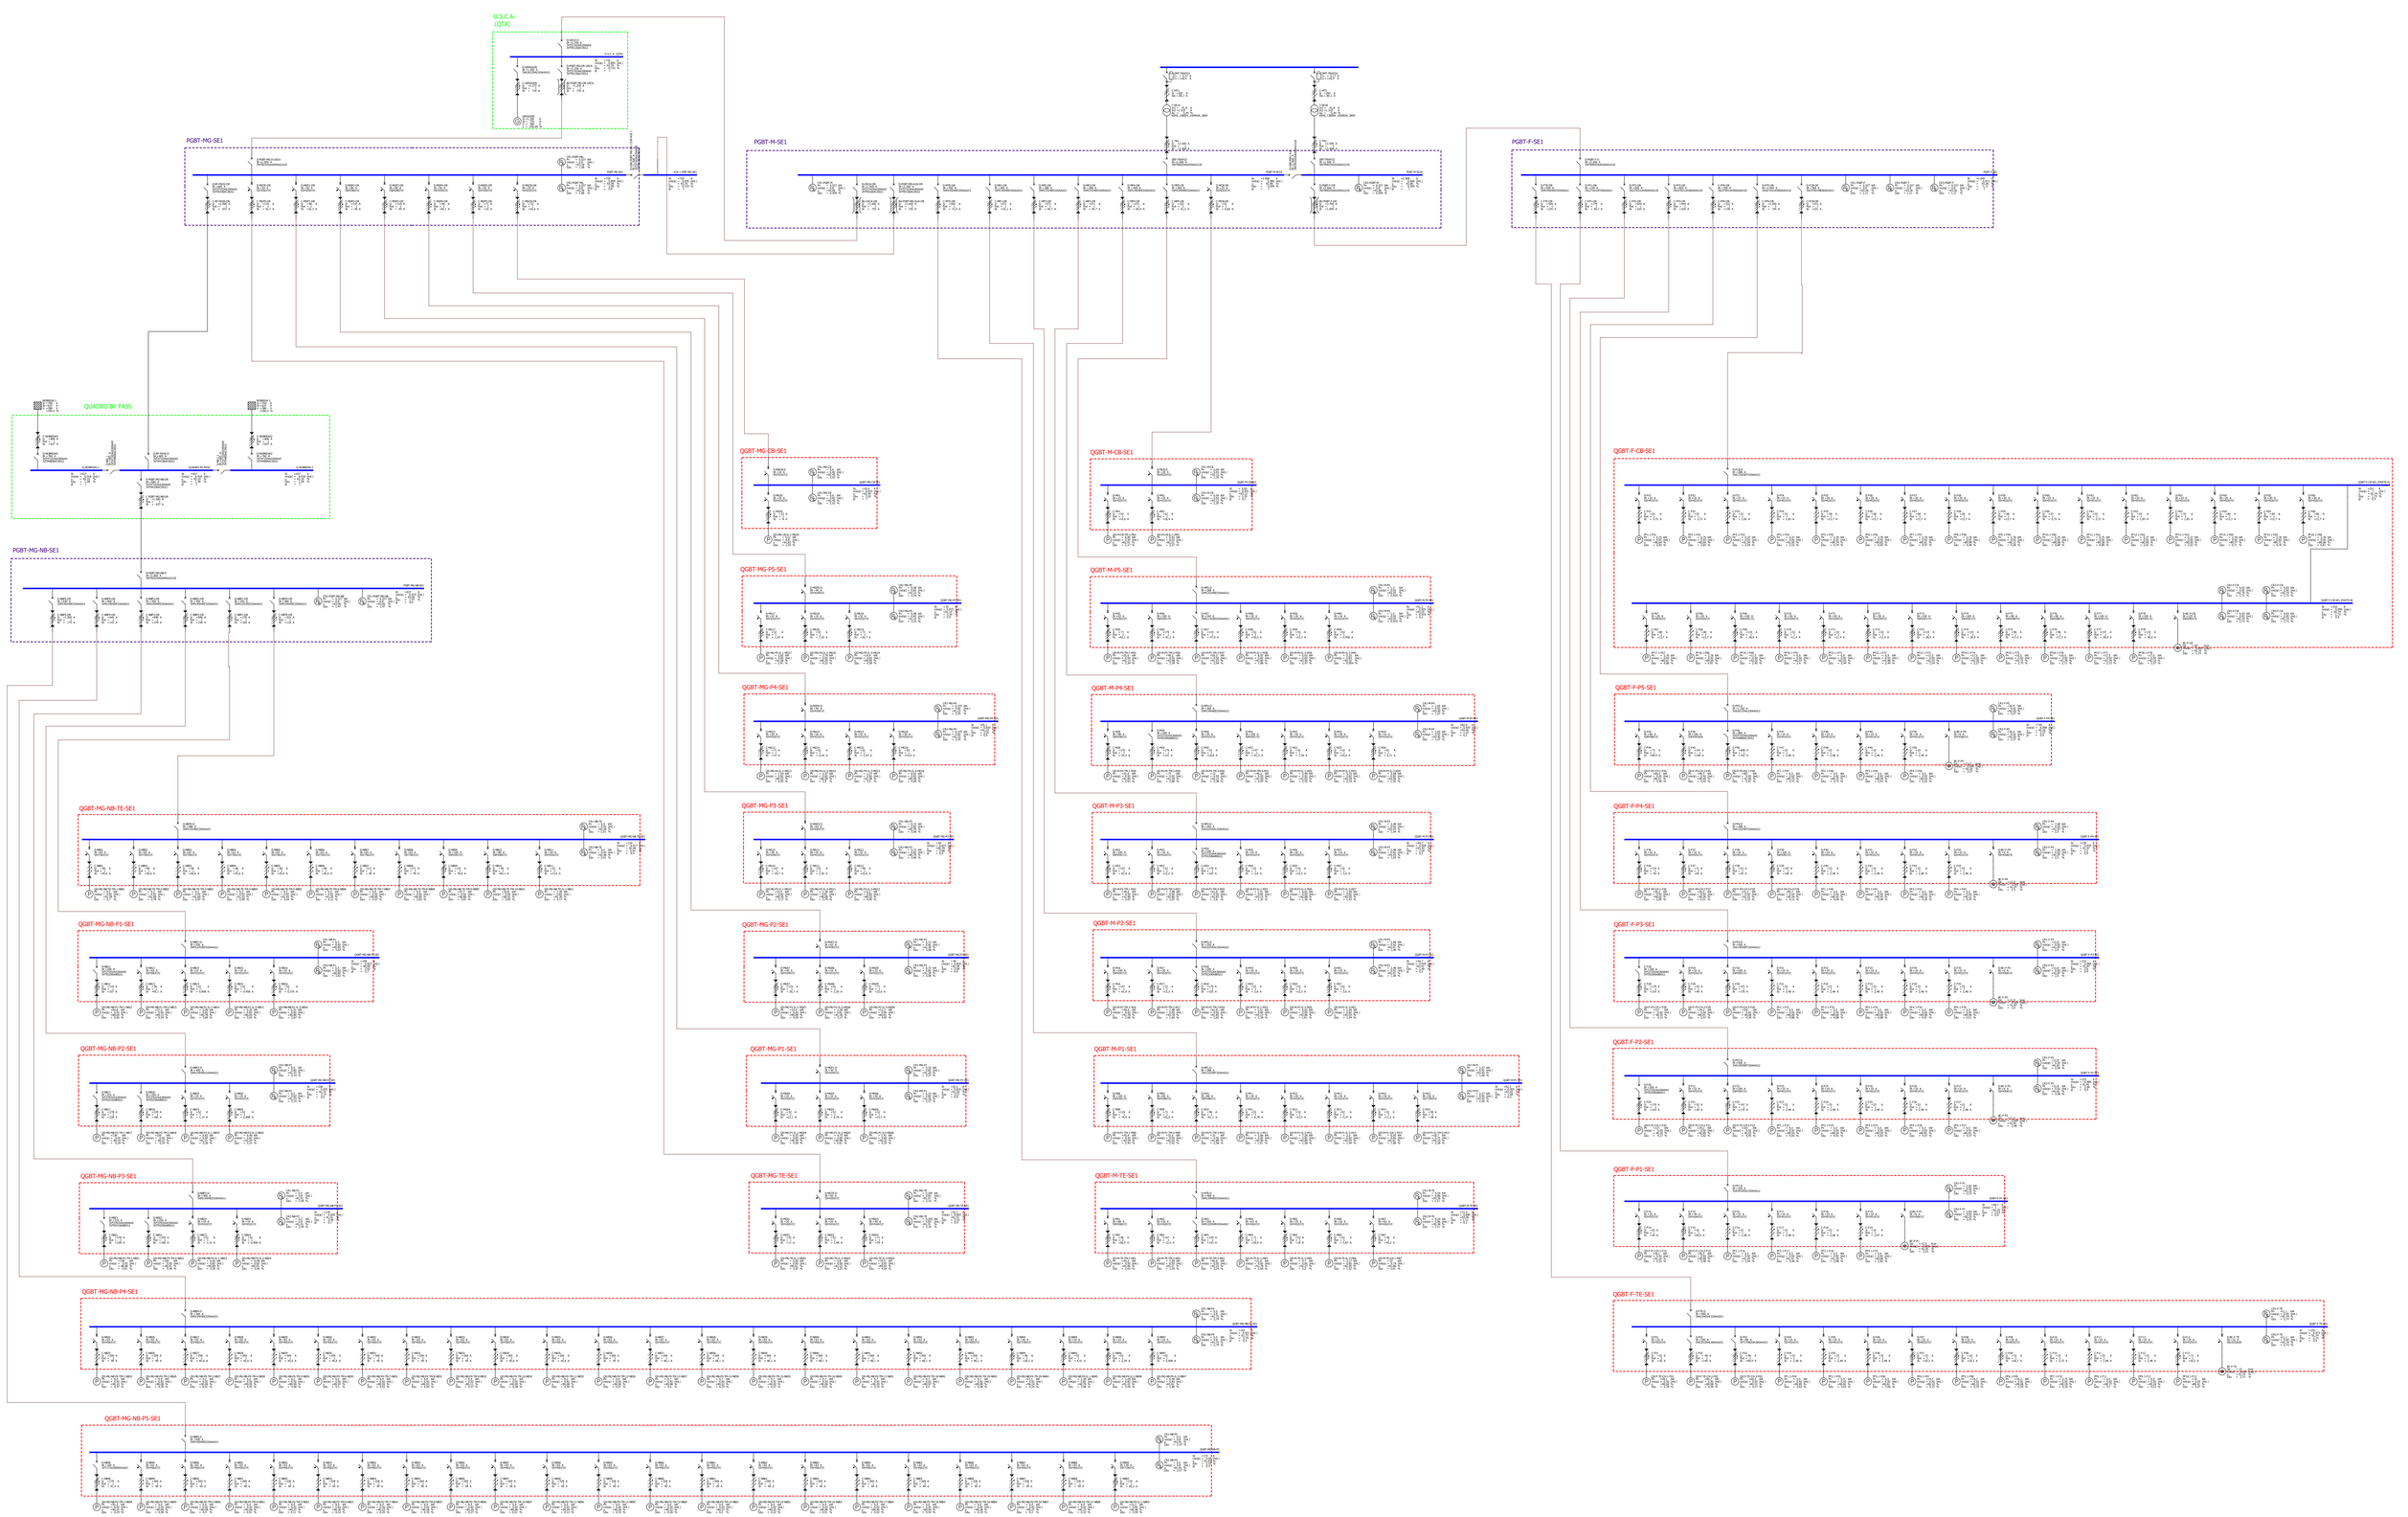

Project name:	Projeto Subestação 8D3U - Ampliação UFU		
Engineer:	Jéssica Cristina	Title: Flowchart distribution	Sheet: 1/1
Design office:	UFU	Location: Uberlândia	
Client:	UFU	Issued: Jun 14, 2023	Printed: Feb 23, 2025

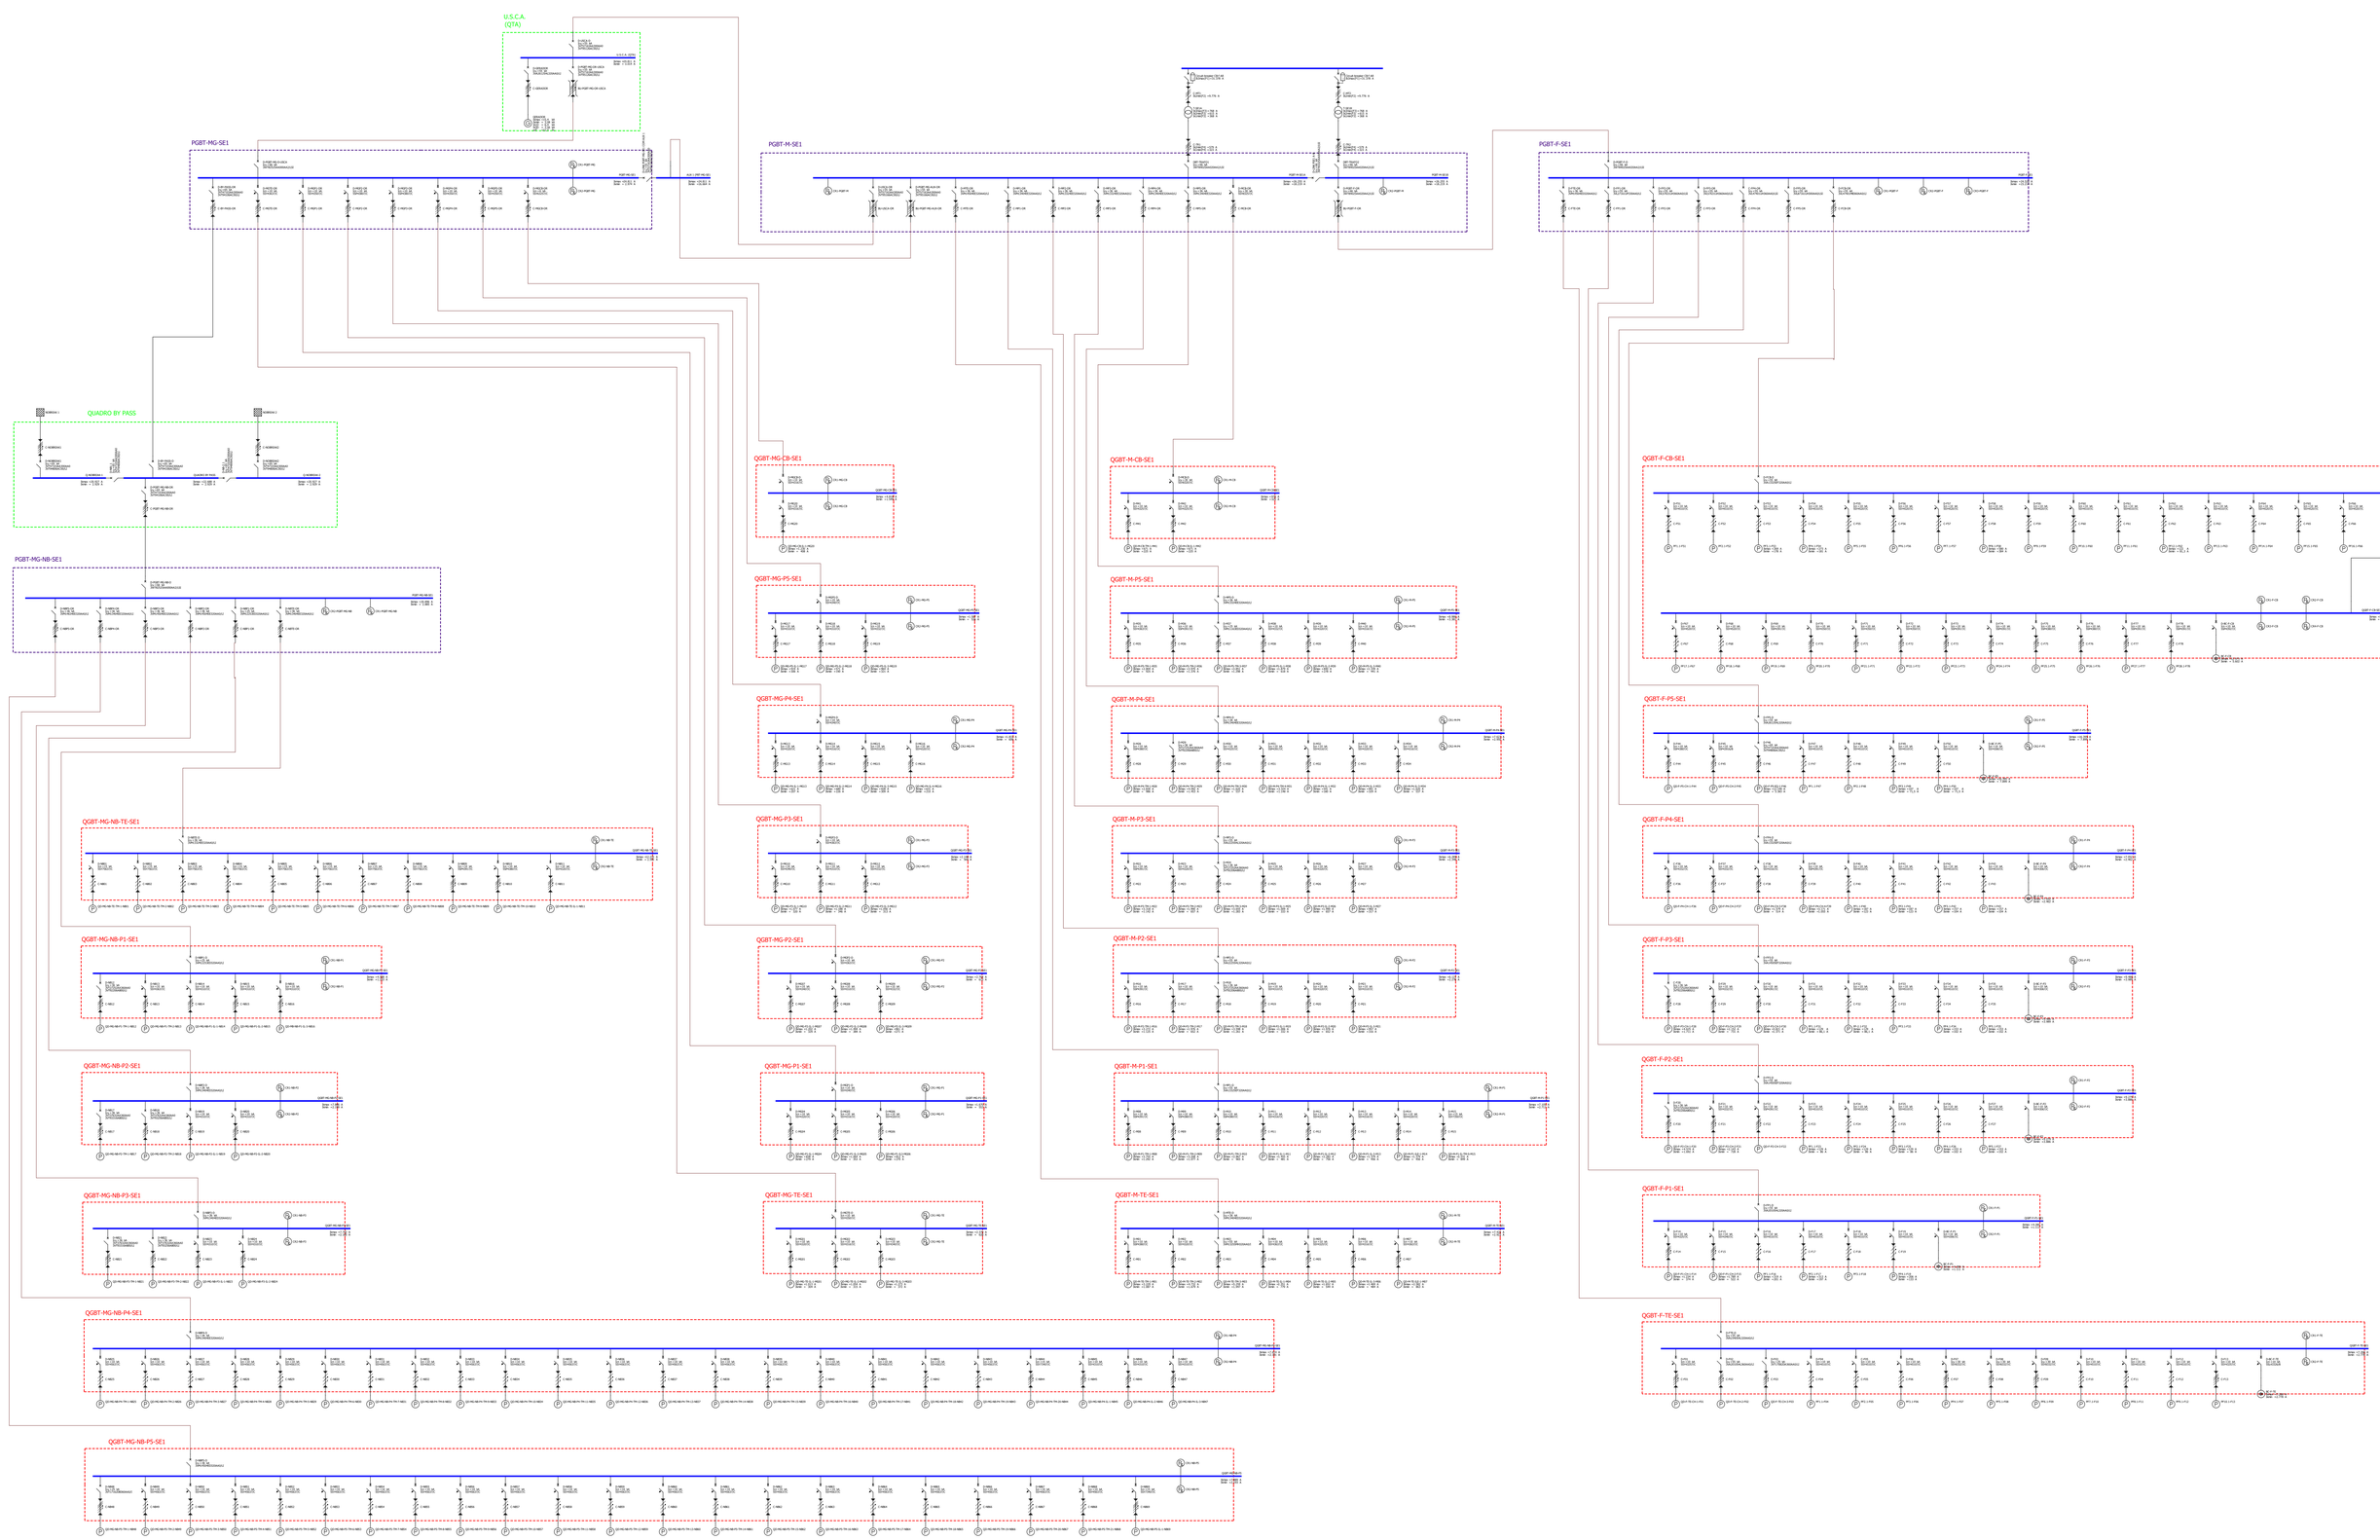

Project name:	Projeto Subestação 88/3U - Ampliação UFU		
Designer:	Jéssica Cristina	Sheet: Short-circuit tweb	Sheet no.: 1/1
Design office:	UFU	Location: Uberlândia	
Client:	UFU	Date: Jun 14, 2023	Printed: Feb 23, 2025

DIPAGE design 12.1.0

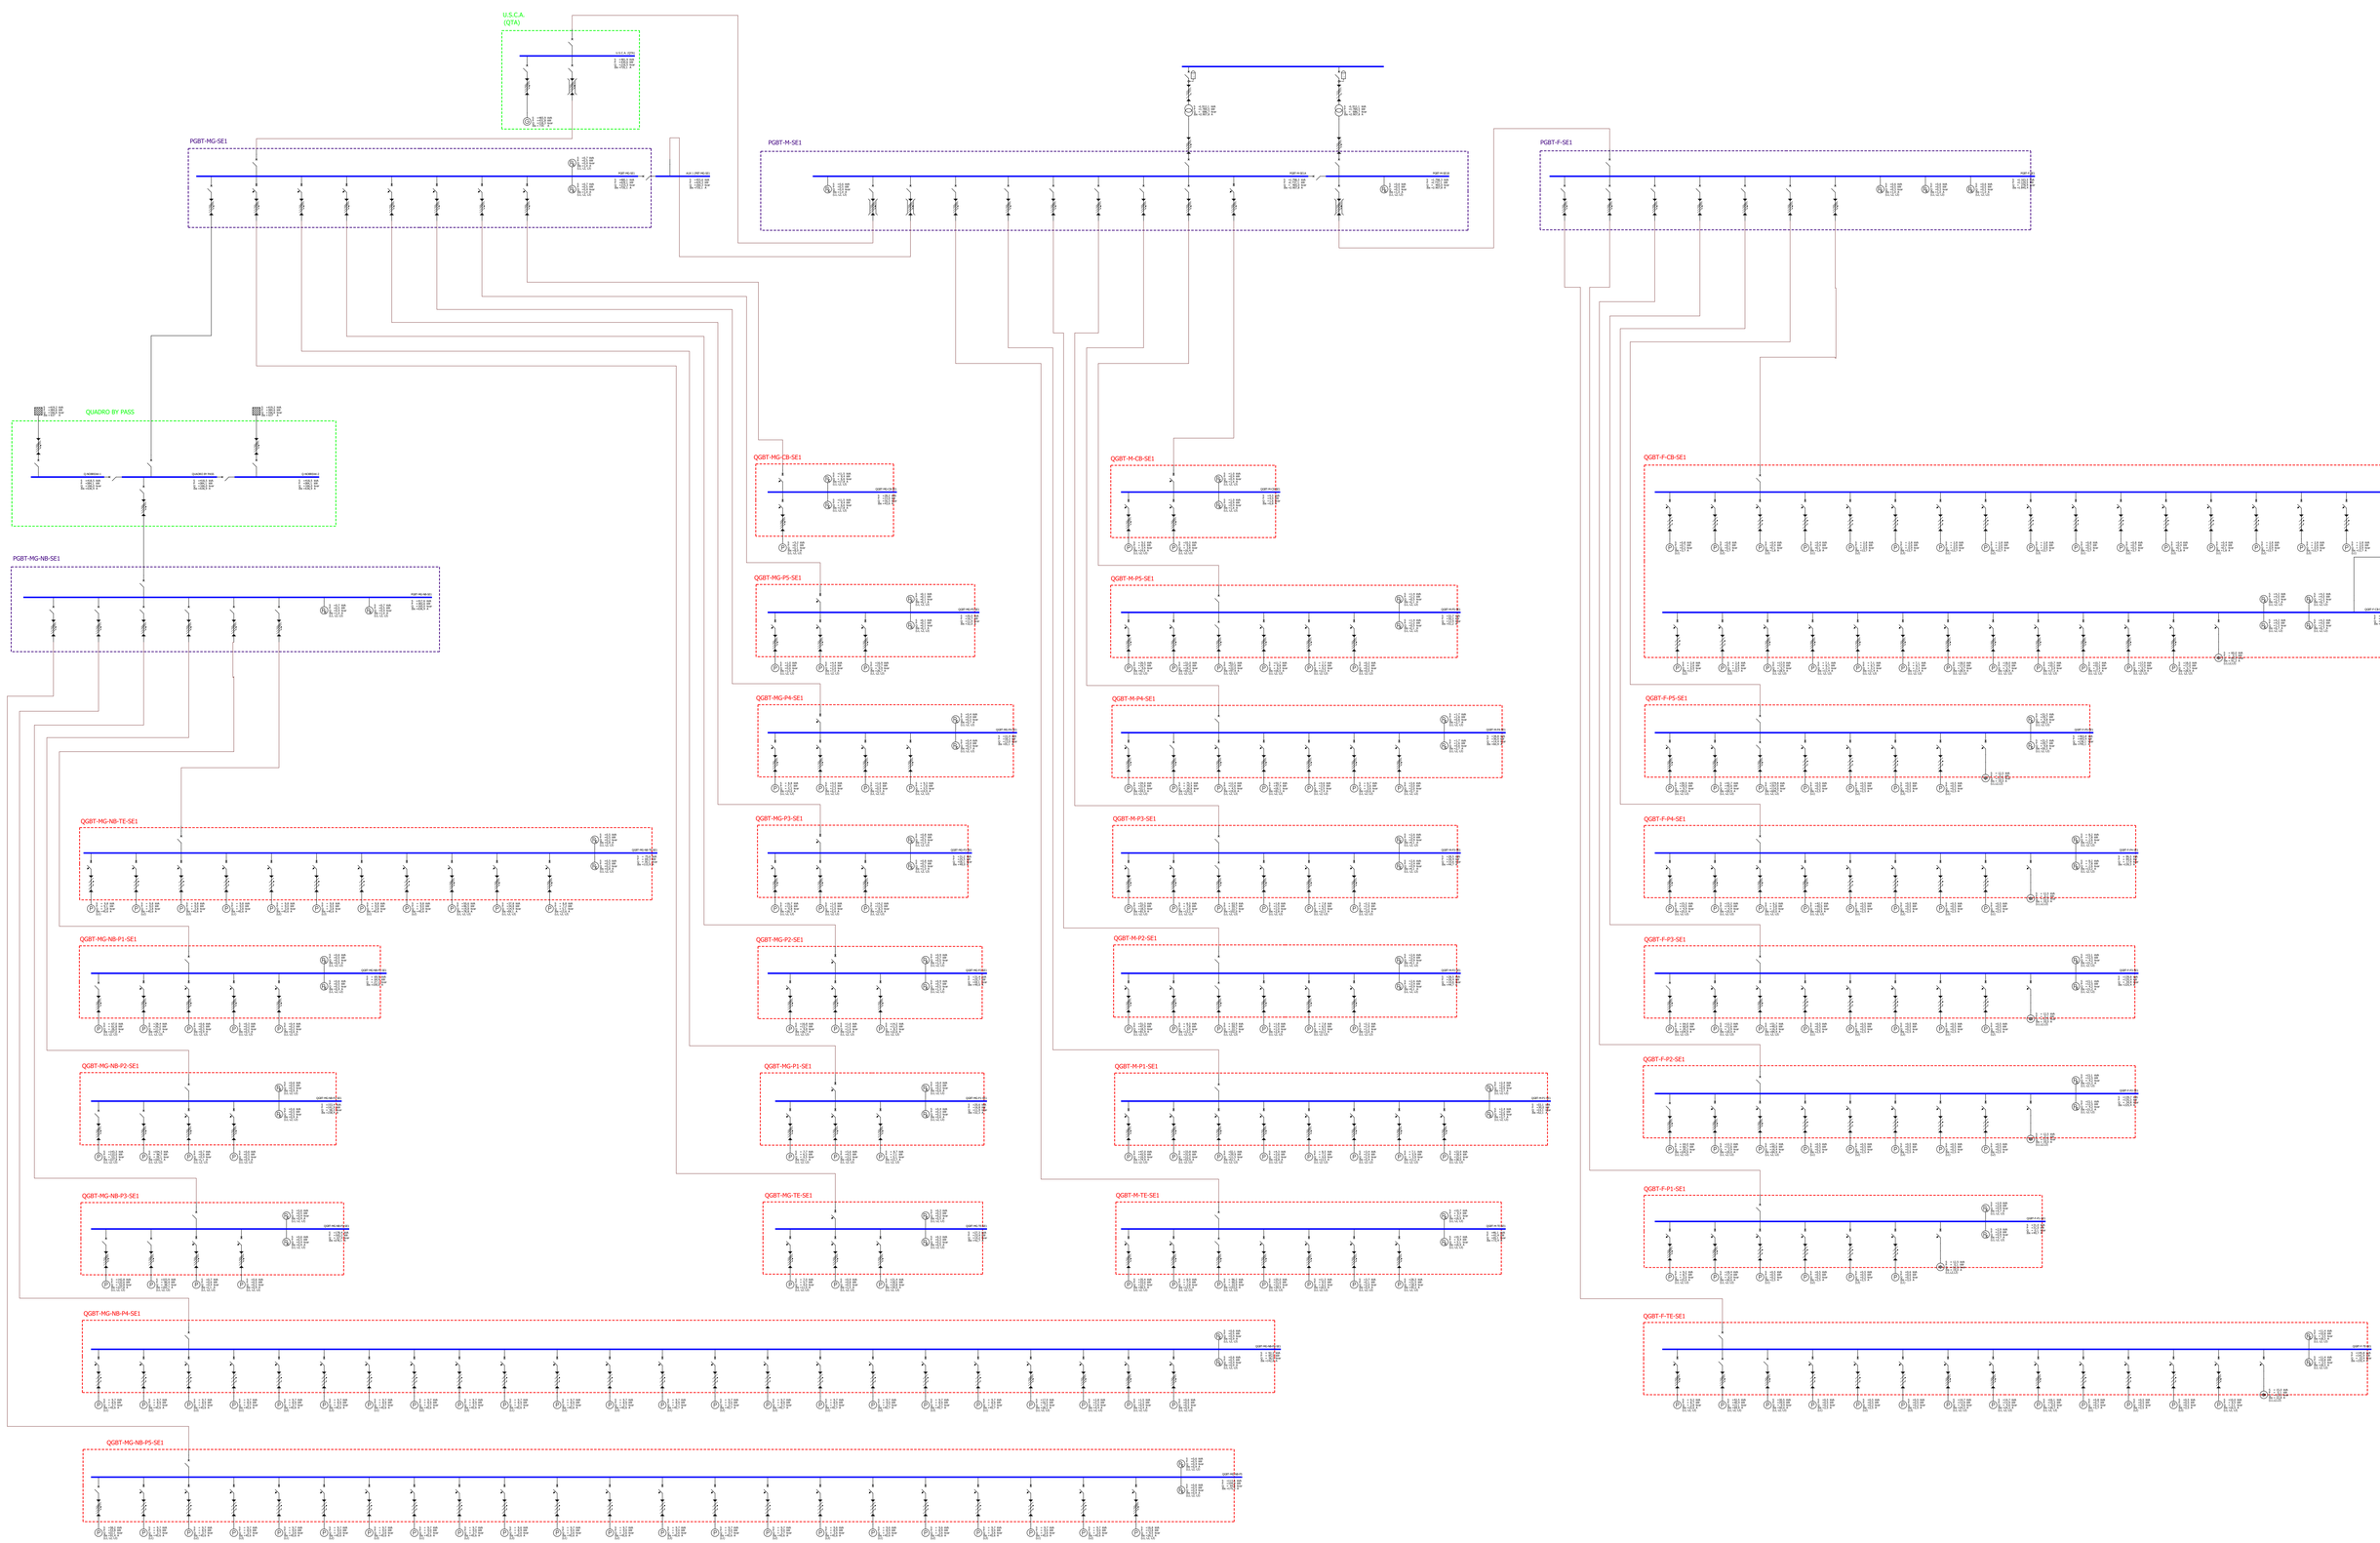

Project name:	Projeto Subestação 88:3U - Ampliação UFU		
Engineer:	Jéssica Cristina	Title: Energy report	Sheet: 1/1
Design office:	UFU	Location: Uberlândia	
Client:	UFU	Created: Jun 14, 2023	Changed: Feb 23, 2025

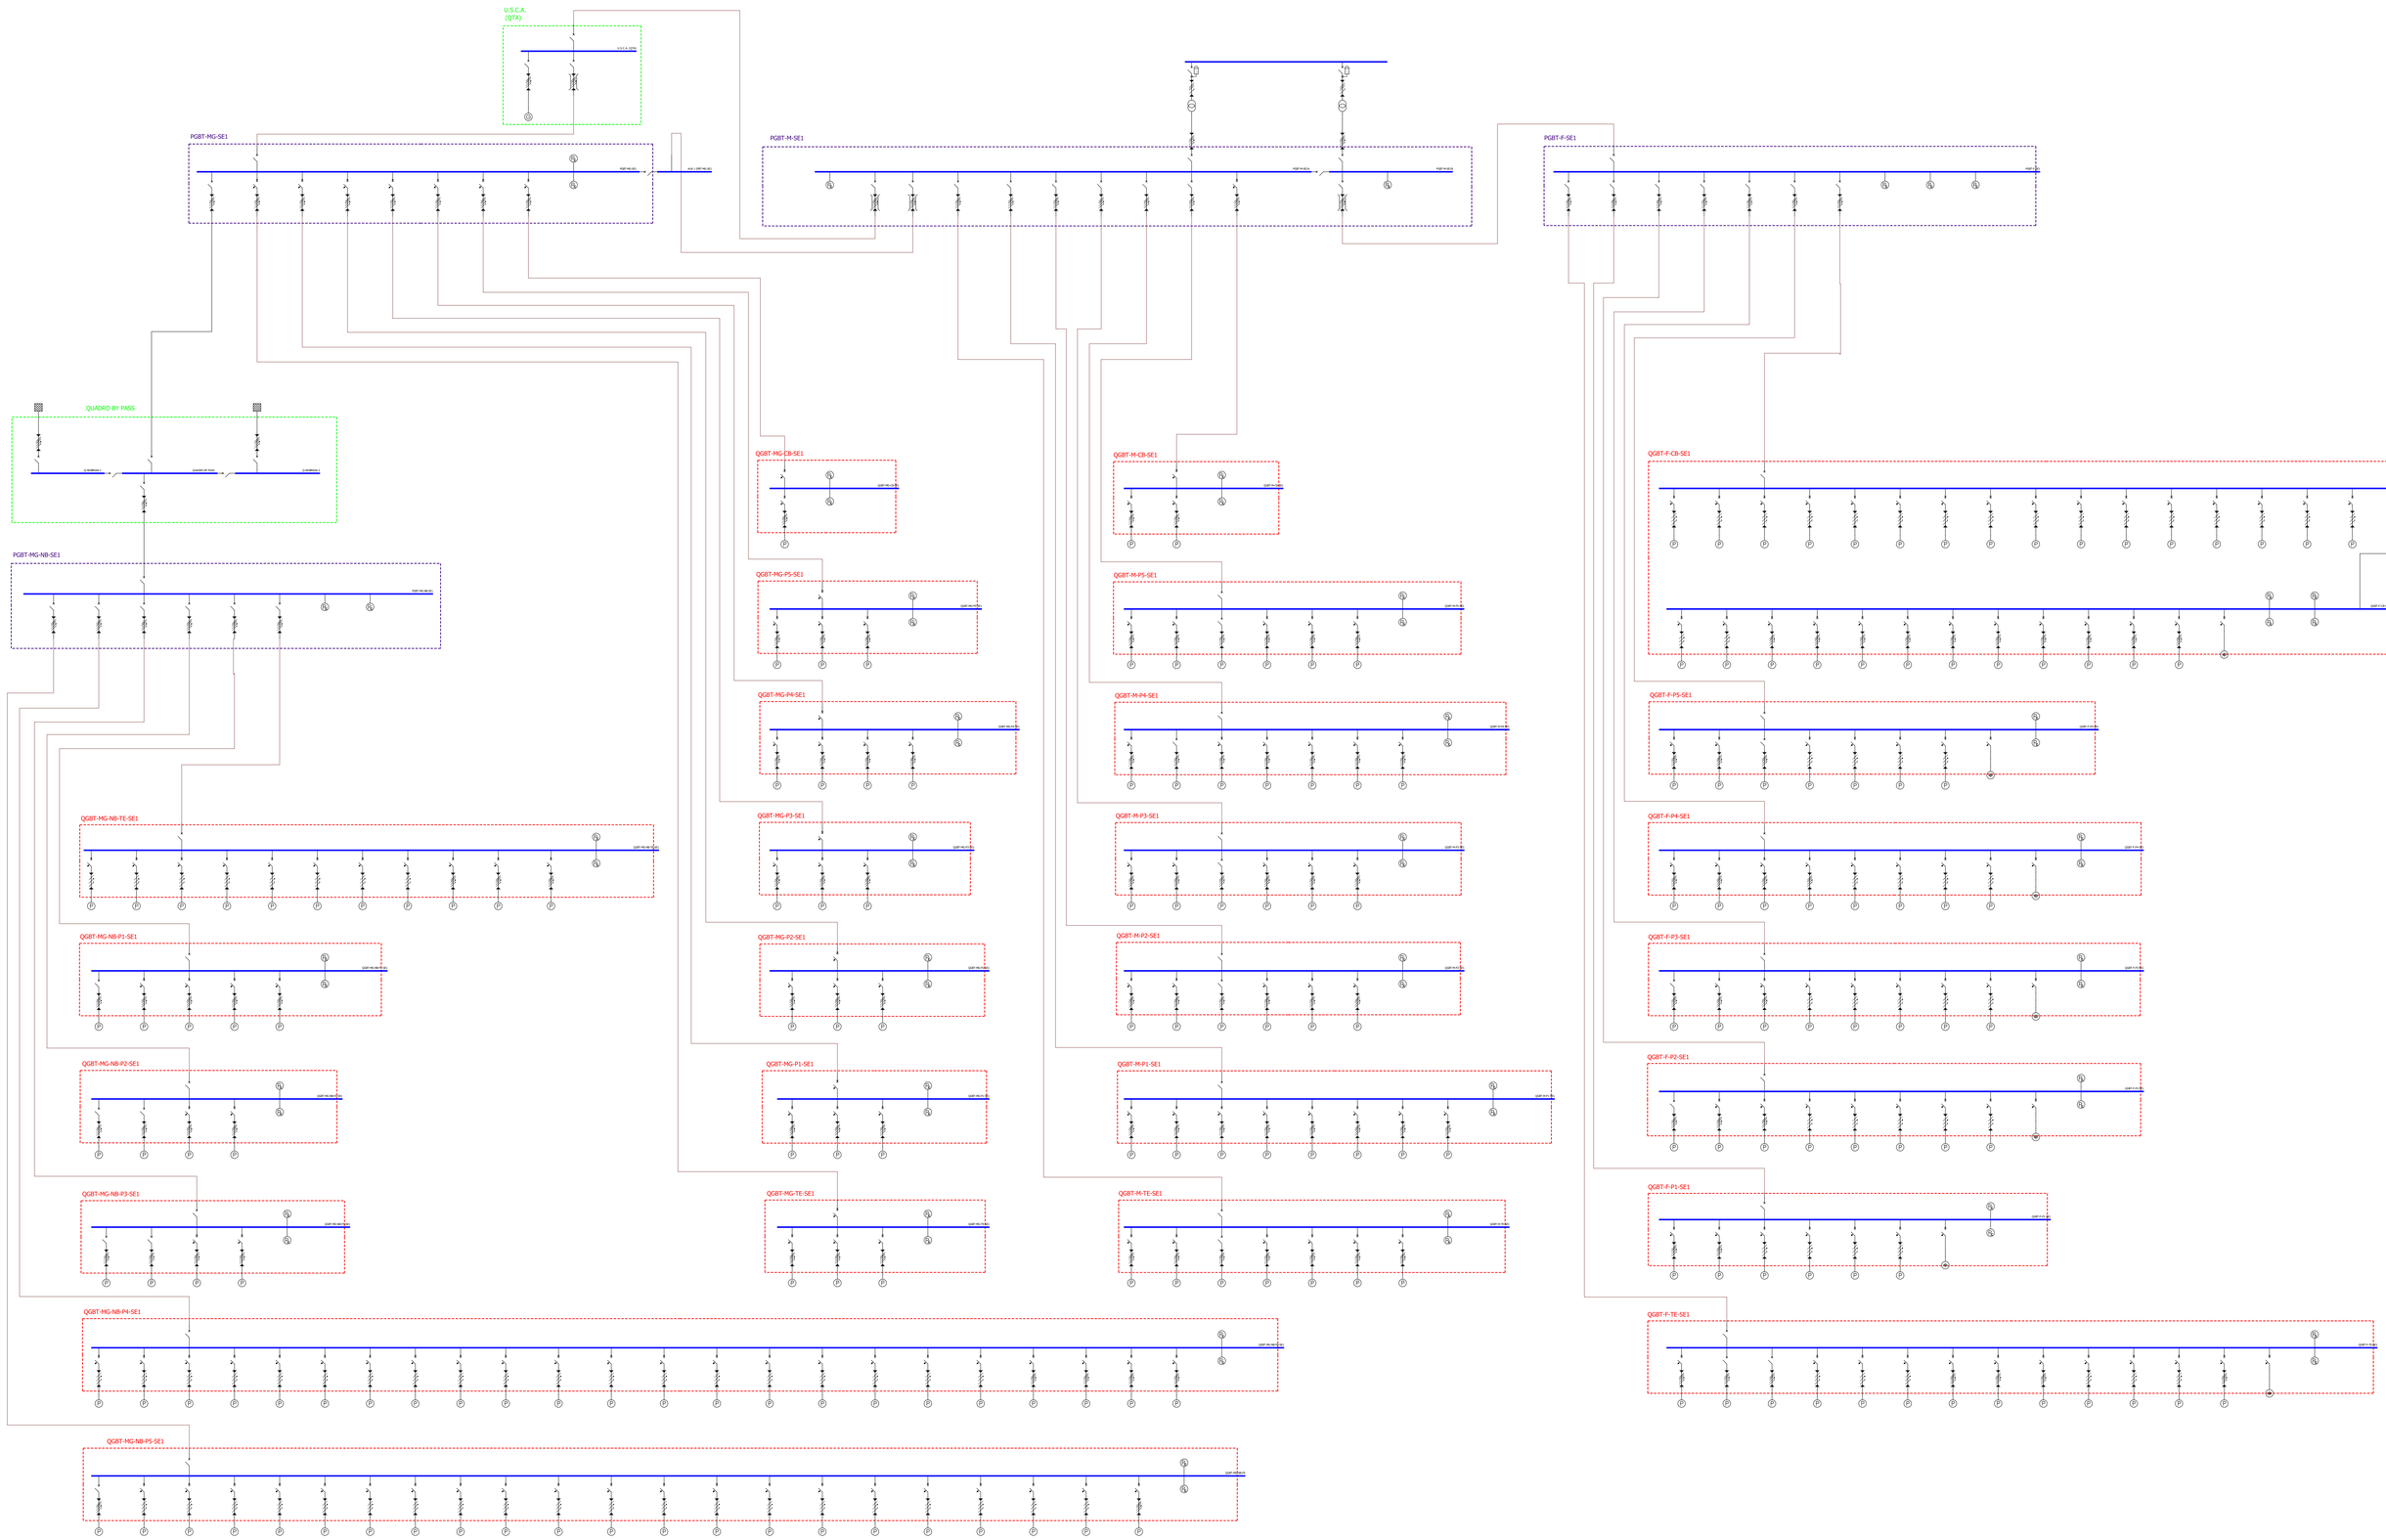

Project name:	Projeto Subestação 8D3U - Ampliação UFU		
Engineer:	Jéssica Cristina	Date:	Sheet: 1/1
Design office:	UFU	Location:	Uberlândia
Client:	UFU	Issued: Jun 14, 2023	Changed: Feb 23, 2025